


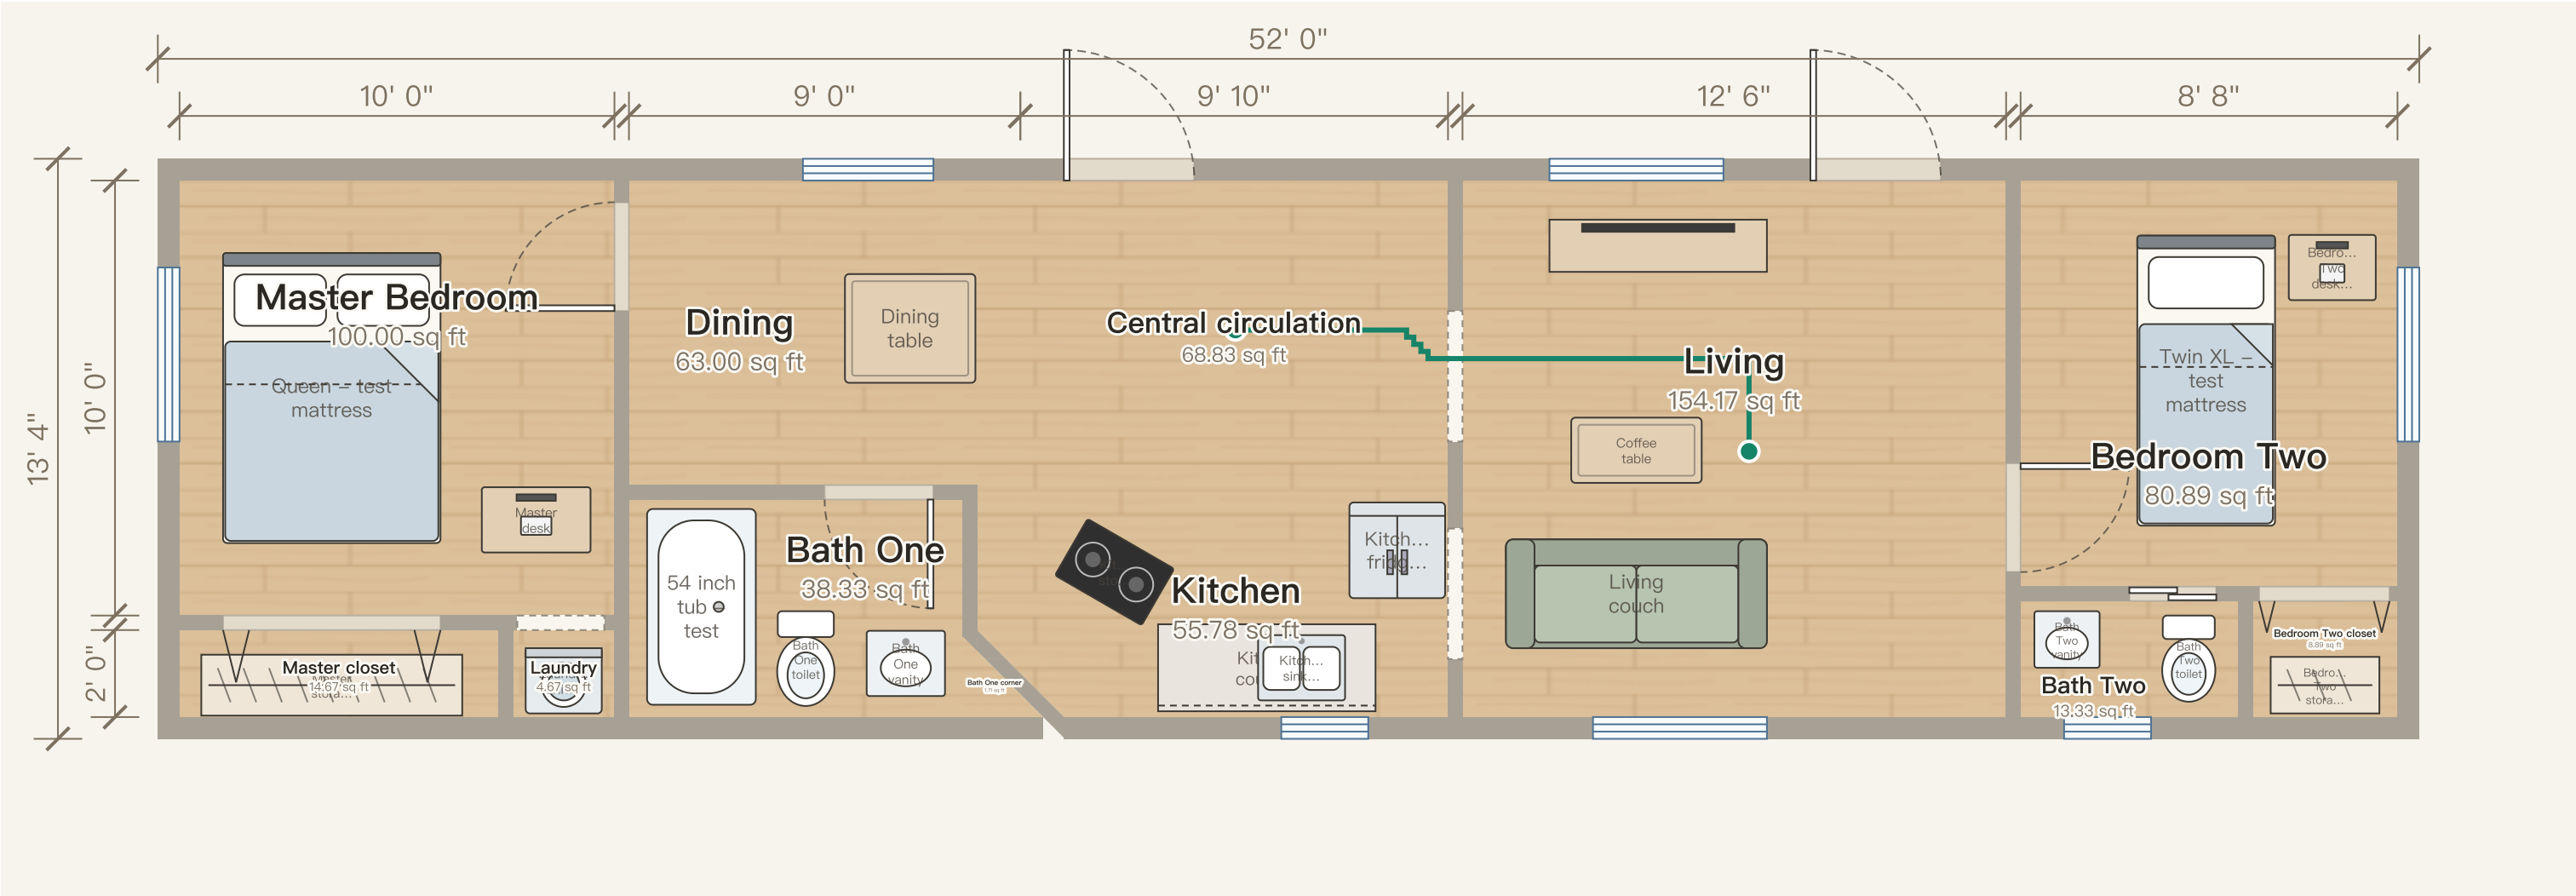

Rooms: 12 · Furniture: 20 · Dashed arcs: door swings · Red sectors: 0 potential door conflicts · Areas use net room dimensions. Passage target: $\approx 1' 11 \frac{5}{8}"$; open door assumption; route-found; Central circulation to Living. Continuous sweep on 50 mm samples; not exact minimum width or whole-home access. Bifold stack dimensions unknown: openings blocked. Diagonal walls: 1. 0 potential floor/boundary conflicts. Footprint area (includes walls): 693.18 sq ft.

